


別見積り

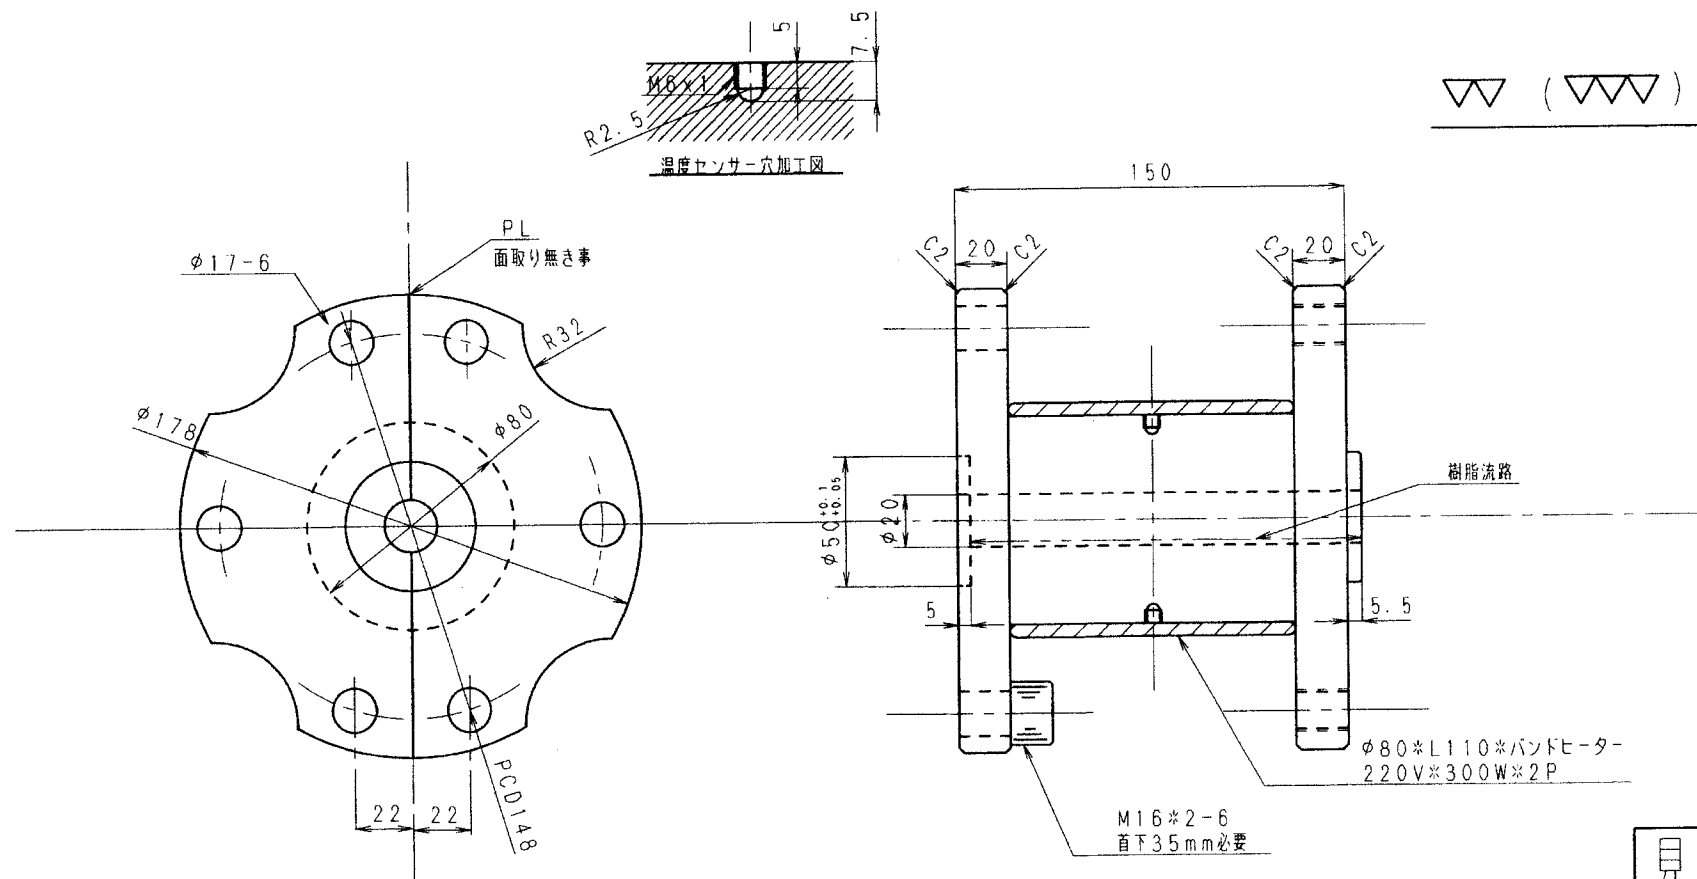

注記

表面処理は、硬質クロムメッキの事
(内壁にも充分なメッキ処理がなされている事)

公差は表面処理後、維持の事

樹脂流路

・段差、キズ、凹凸無き事

指示なき角部は糸面取りの事
(但し樹脂流路は除く)

見積用

名称：E4 40用角ノズル図

5				SCALE 1:2	DATE 22.3.9	THIRD ANGLE PROJECTION
4				QUANTITY 1式	MATERIAL S55C	DWG. SIZE A3
3				TITLE EXT40用		PART No.
2						
1						
REVISION RECORD				DATE	BY	APPR
APPROVED BY				CHECKED BY	DESIGNER	